
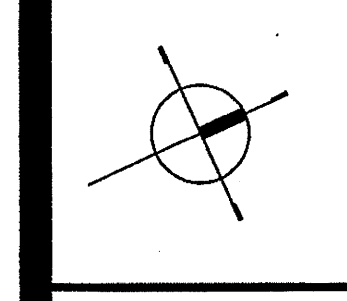


GENERAL NOTES

- THIS PLAN IS FOR DIMENSIONAL PURPOSES ONLY.
- GENERAL CONTRACTOR TO NOTIFY ARCHITECT AFTER LAYOUT IS DONE AND WALL TRACK IS IN PLACE PRIOR TO FRAMING ANY WALLS.
- FOR DIMENSIONING PURPOSES, METAL STUDS ARE DRAWN AT 4" OR 6" U.O.N. AND BLOCK WALLS ARE DRAWN AT 8" U.O.
- 8" BLOCK WALLS AND 6" METAL STUD WALLS ARE DIMENSIONED AT FACE OF WALL AND 4" METAL STUD WALLS ARE DIMENSIONED AT CENTER OF WALL U.O.

REVISIONS	BY
1	02.11.07 DC

OLIVERI ARCHITECTS
 A.A. 0002021
 Member of the American Institute of Architects
 32707 US Hwy. 19 • Palm Harbor, FL 34684
 Phone: 727.781.7525 • Fax: 727.781.6925 • E-mail: design@oliveriarch.com

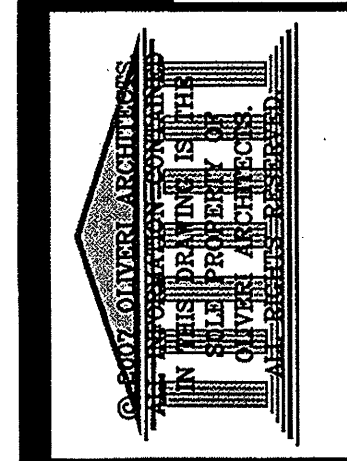

Joseph L. Oliveri
 9-20-07
 Joseph L. Oliveri, AIA
 A10014028

HERNANDO CO. DEVELOPMENT SERVICES DEPARTMENT

Building Plans Review	
Approved for Use	<input checked="" type="checkbox"/> Not Approved
Approved as Noted	<input type="checkbox"/> Comments Attached

This review does not relieve the Contractor from errors or omissions in this submittal or from the Contractor's responsibility for code compliance. These plans have been reviewed for code compliance in accordance with the Florida Building Code. The issuance of this permit shall not be held to permit or approve the violation of any law, code regulation or ordinance.

Date: OCT 18 2007

A-ZONE

JOB COPY

1211883-

RECEIVED
 SEP 21 2007
 HERNANDO COUNTY
 DEVELOPMENT DEPT.

New Free Standing Retail Center
SHOPPES OF SPRING HILL
 1859 Commercial Way
 Spring Hill, Florida

Date: 06. 11. 07
 Scale: AS NOTED
 Project Mgr: GD
 Drawn: SEH
 Job: 07-23

Sheet
A1b

DIMENSIONED FLOOR PLAN
 SCALE: 1/8" = 1'-0"